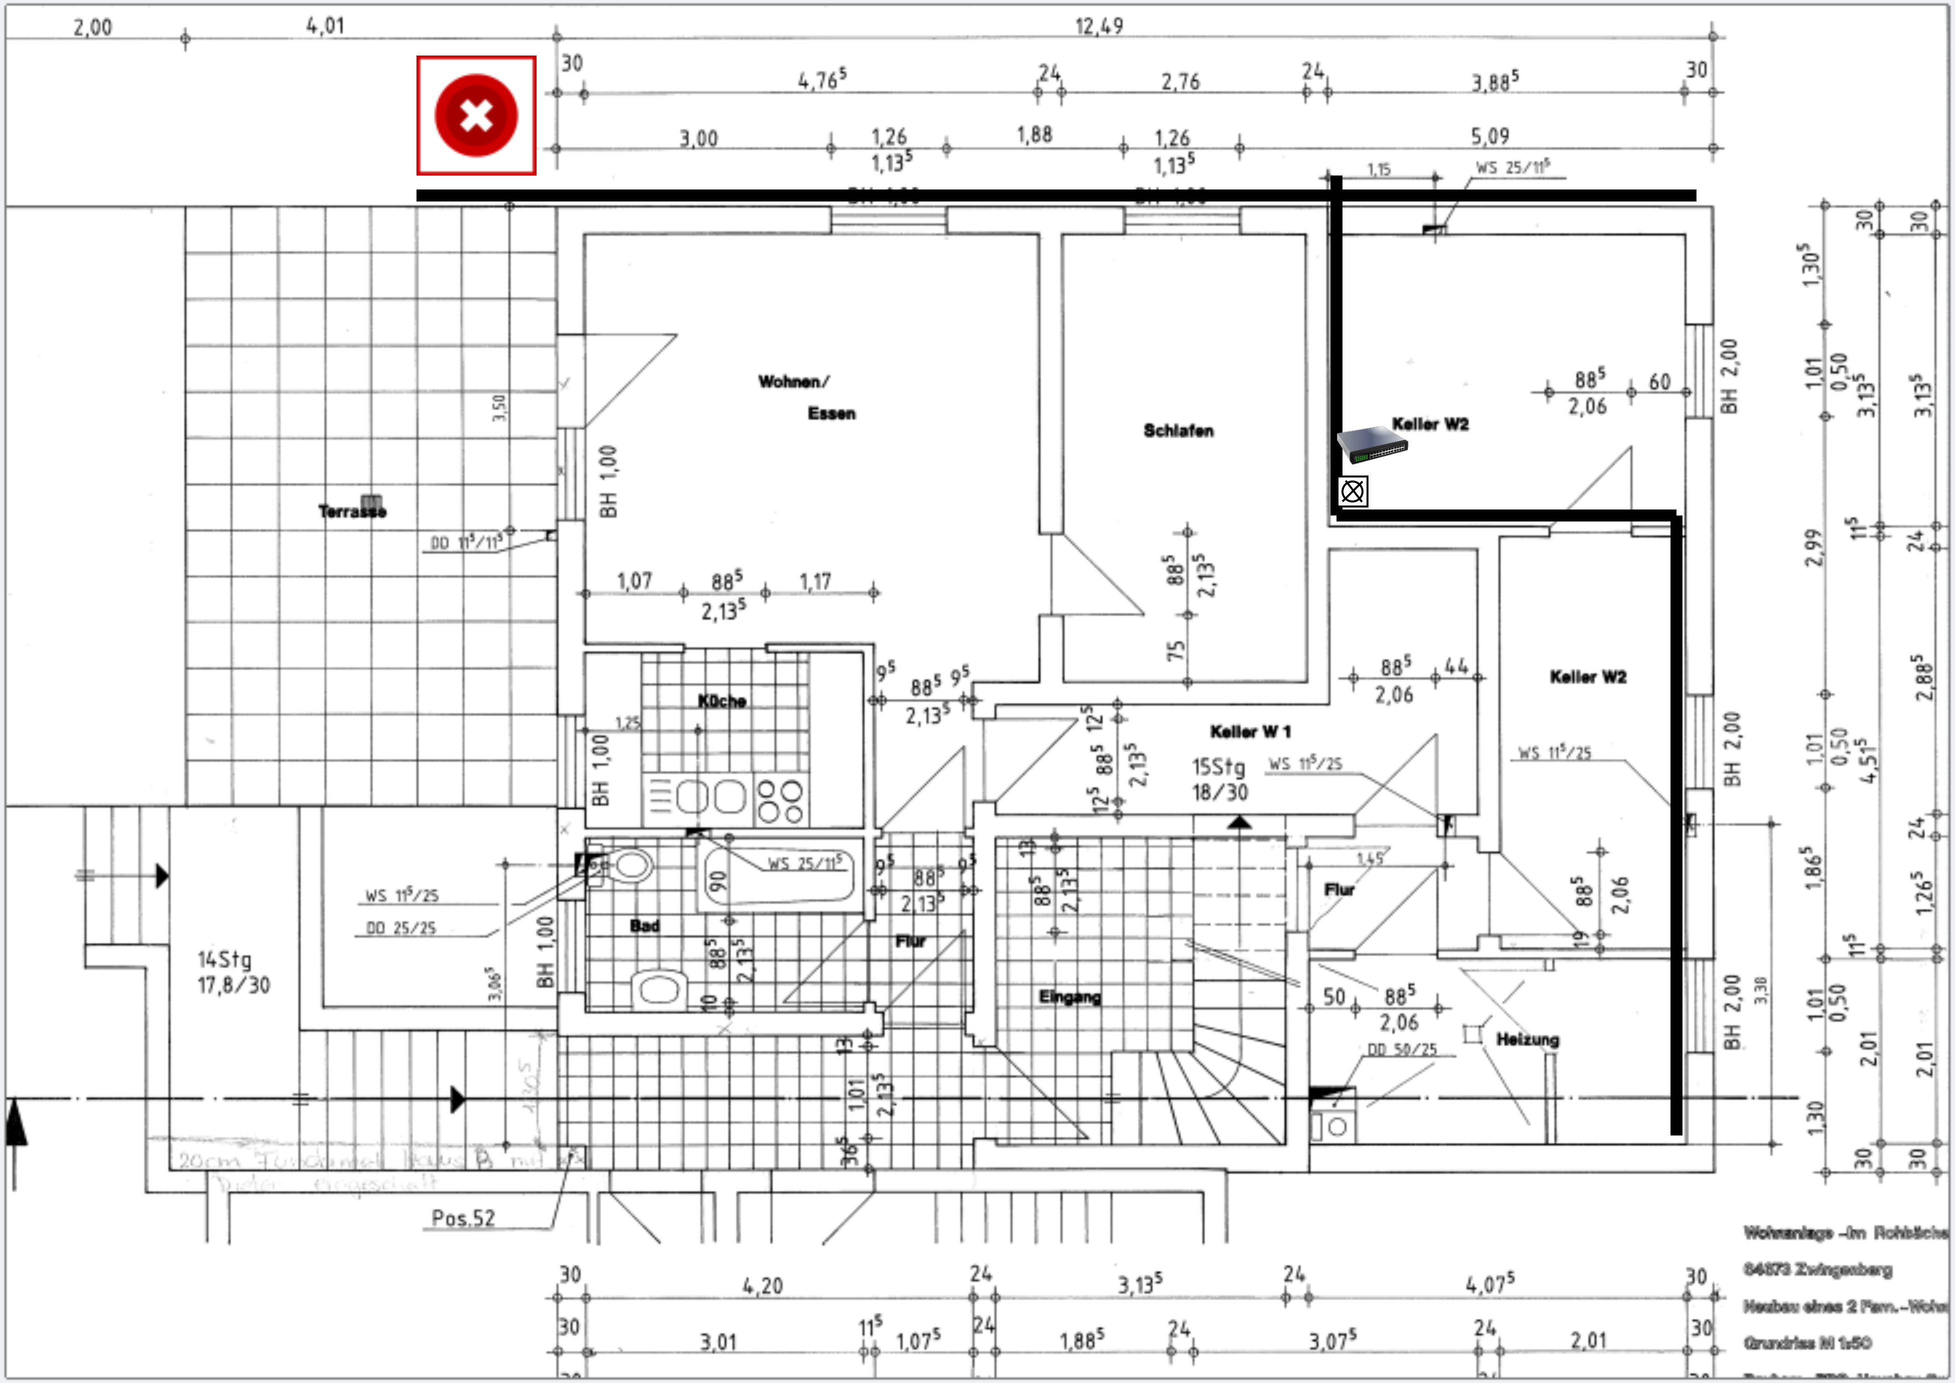
2,00
4,01
12,49
30
4,76⁵
24
2,76
24
3,88⁵
30
3,00
1,26
1,13⁵
1,88
1,26
1,13⁵
5,09
1,15
WS 25/11⁵
Wohnen/
Essen
Schlafen
Keller W2
Terrasse
3,50
DD 11⁵/11⁵
BH 1,00
1,07
88⁵
1,17
2,13⁵
88⁵
2,13⁵
75
88⁵
60
2,06
BH 2,00
Küche
1,25
BH 1,00
9⁵
88⁵
9⁵
2,13⁵
12⁵
88⁵
2,13⁵
12⁵
Keller W 1
15Stg
18/30
WS 11⁵/25
88⁵
44
2,06
Keller W2
WS 11⁵/25
BH 2,00
WS 25/11⁵
90
9⁵
88⁵
9⁵
2,13⁵
13
88⁵
2,13⁵
1,45
Flur
88⁵
2,06
19
Bad
Flur
Eingang
WS 11⁵/25
DD 25/25
3,06⁵
BH 1,00
88⁵
2,13⁵
10
14Stg
17,8/30
50
88⁵
2,06
DD 50/25
Heizung
BH 2,00
3,38
13
1,01
2,13⁵
36⁵
1,30⁵
20cm Fundament Haus B mit Dielen eingeschalt
Pos.52
30
4,20
24
3,13⁵
24
4,07⁵
30
30
3,01
11⁵
1,07⁵
24
1,88⁵
24
3,07⁵
24
2,01
30
30
1,30⁵
1,01
0,50
3,13⁵
2,99
11⁵
1,01
0,50
4,51⁵
1,86⁵
1,01
0,50
2,01
1,30
30
30
24
2,88⁵
24
1,26⁵
11⁵
2,01
30

Wohnanlage –Im Rohbäche

64673 Zwingenberg

Neubau eines 2 Fam.-Woh

Grundriss M 1:50
]